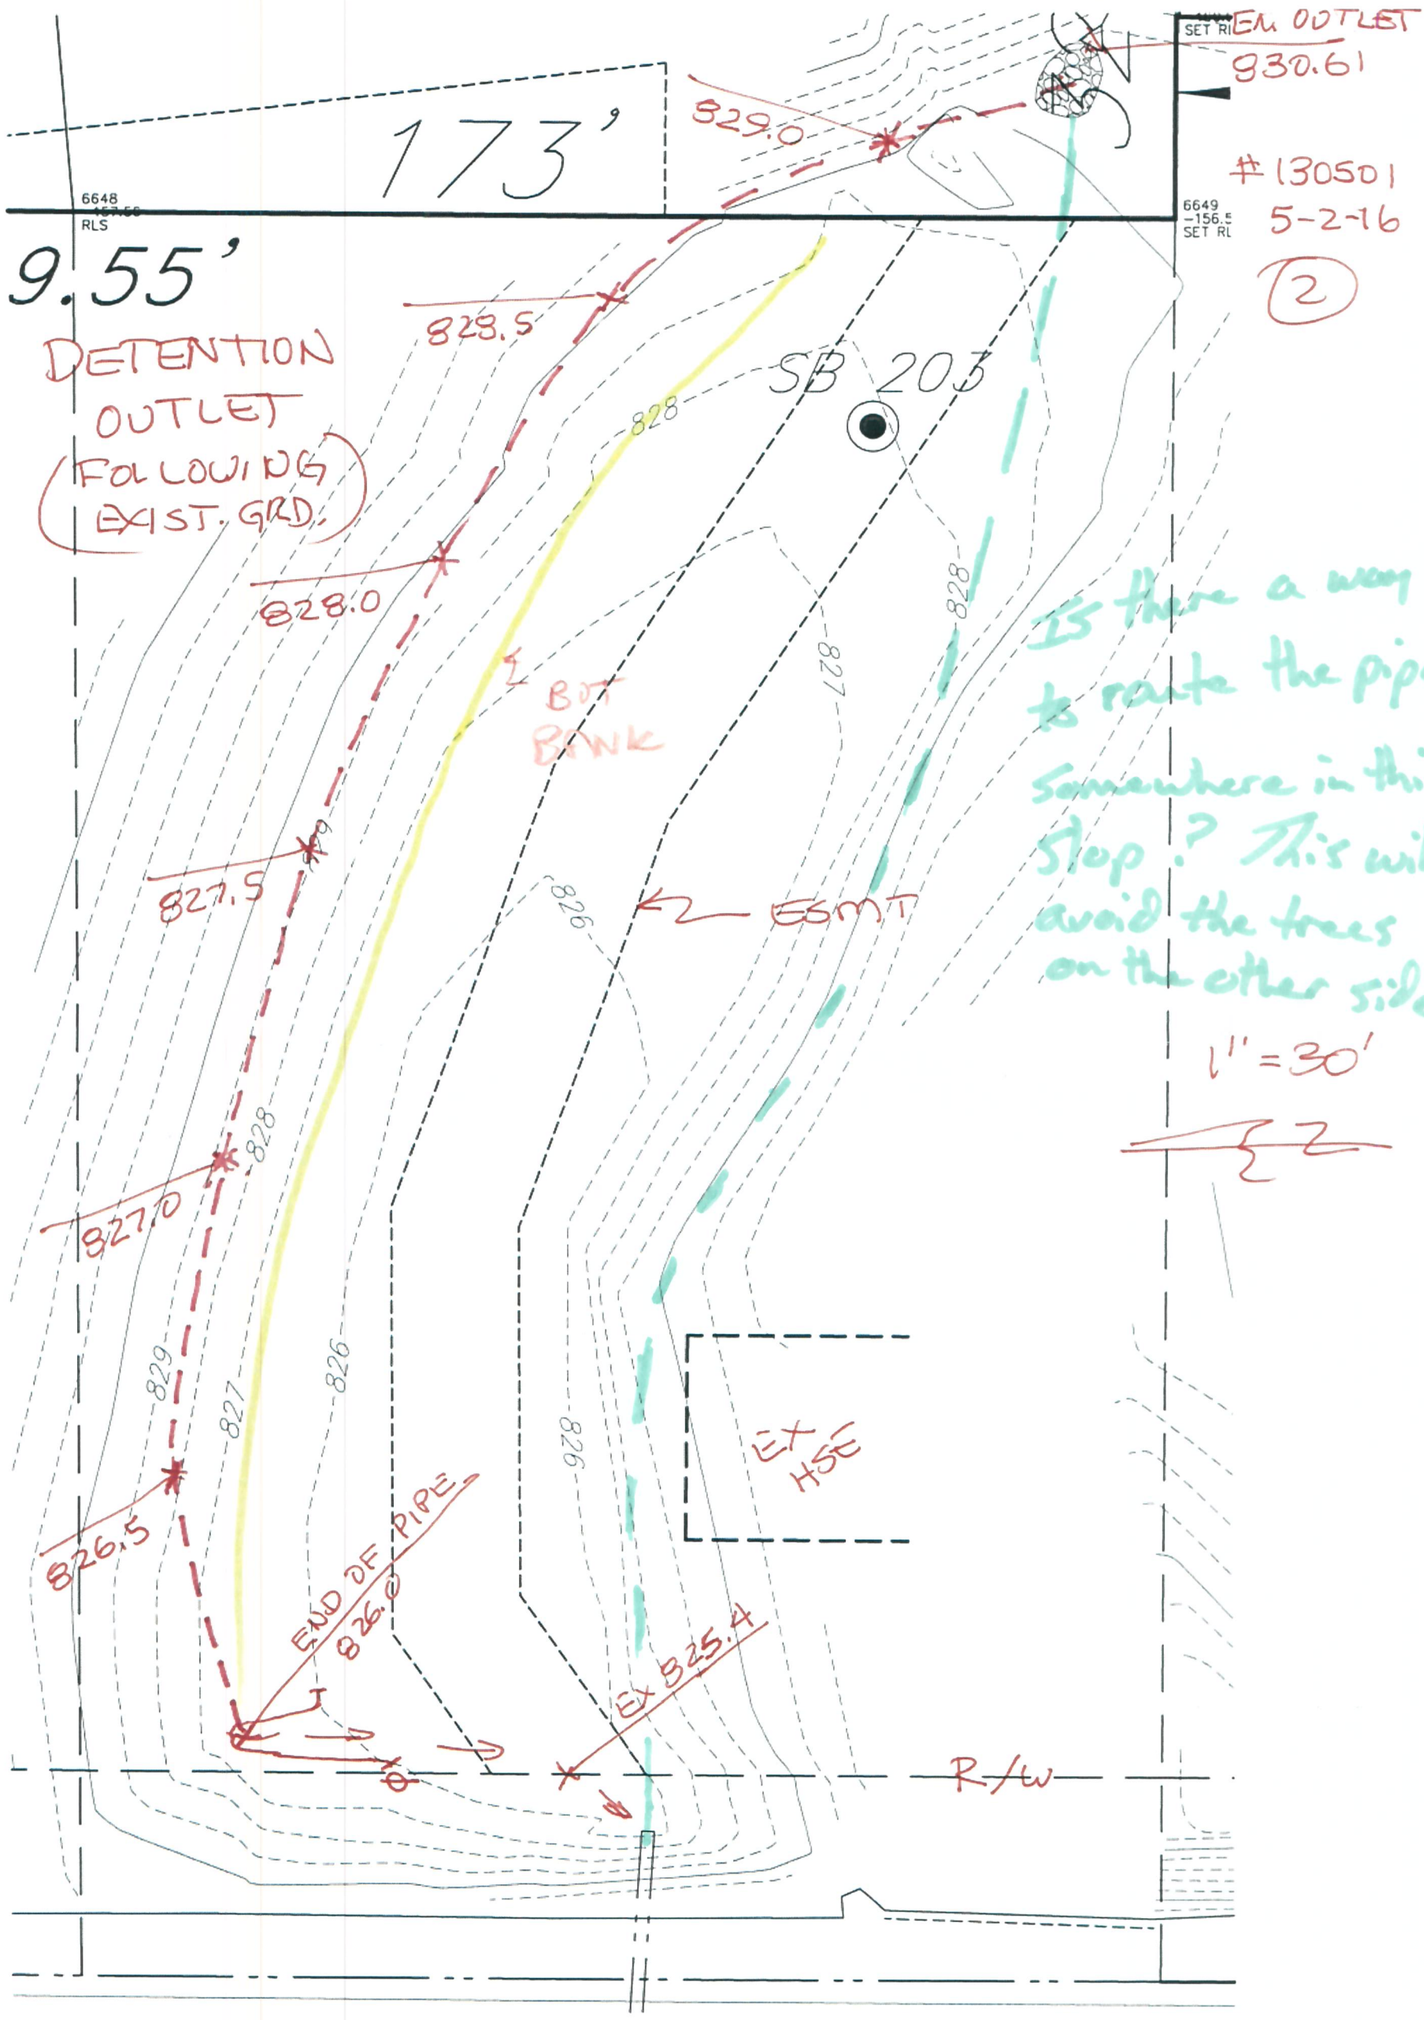
EM OUTLET
830.61
#130501
5-2-16
2
173'
9.55'
829.0
828.5
828.0
827.5
827.0
826.5
DETENTION OUTLET (FOLLOWING EXIST. GRD.)
SB 203
BOT BANK
ESMT
EX HSE
END OF PIPE 826.0
EX 825.4
R/W
828
827
826
829
Is there a way to route the pipe somewhere in this slop? This will avoid the trees on the other side.
1" = 30'