TE CONDOMINIUM
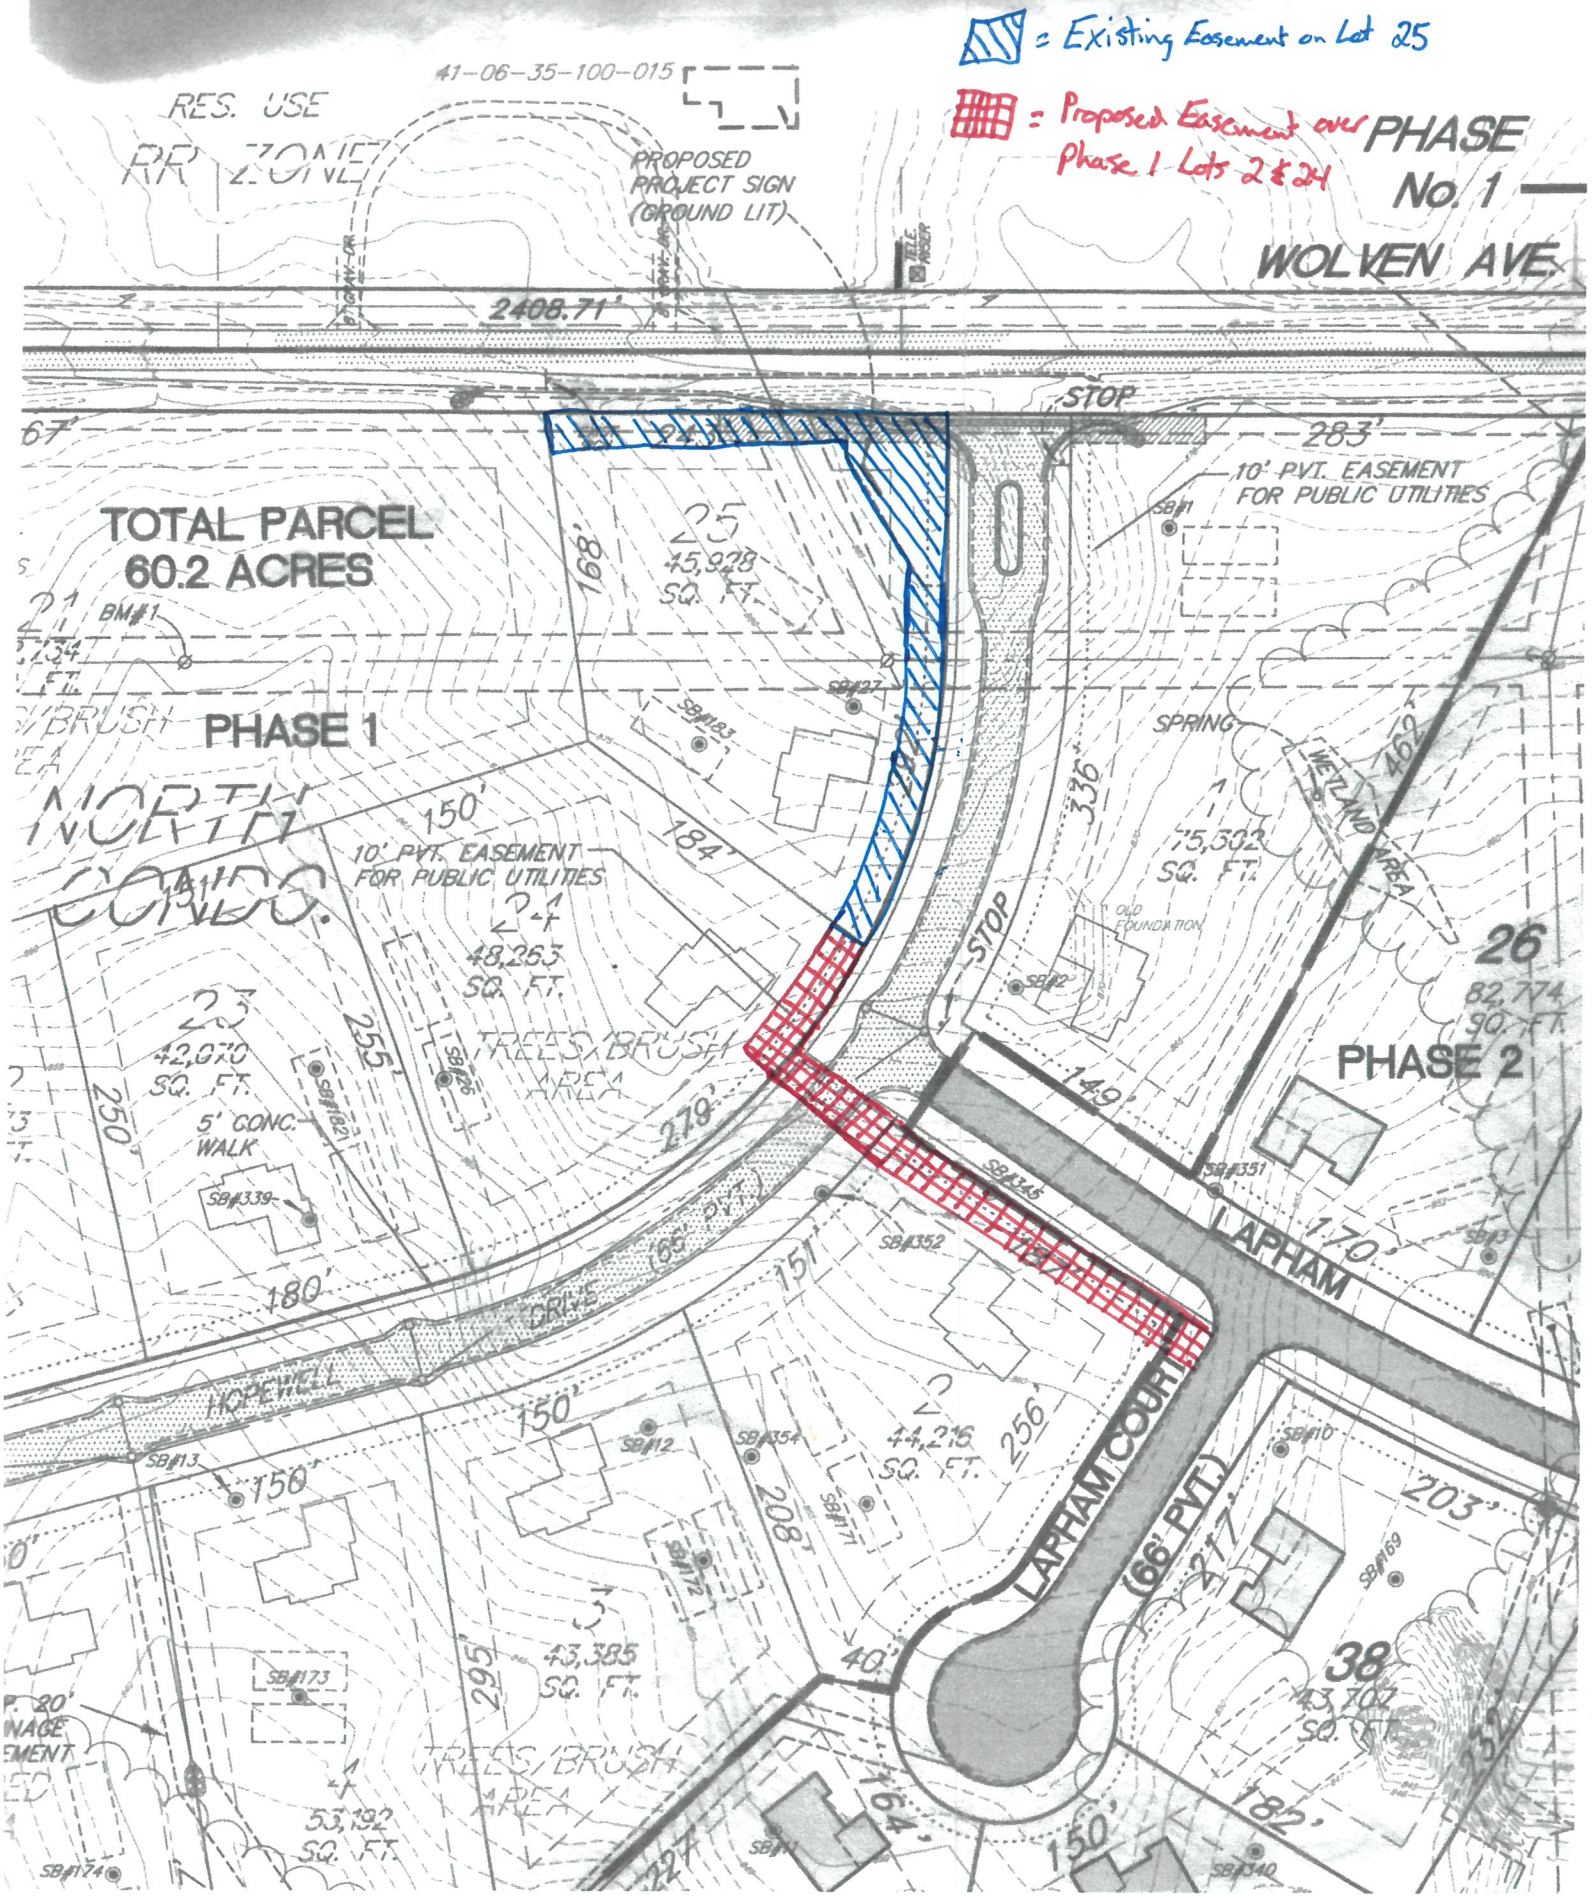
NSTRUCTION PLAN