"43 NORTH" SITE CONDOMINIUM

PHASE #2 CONSTRUCTION PLAN

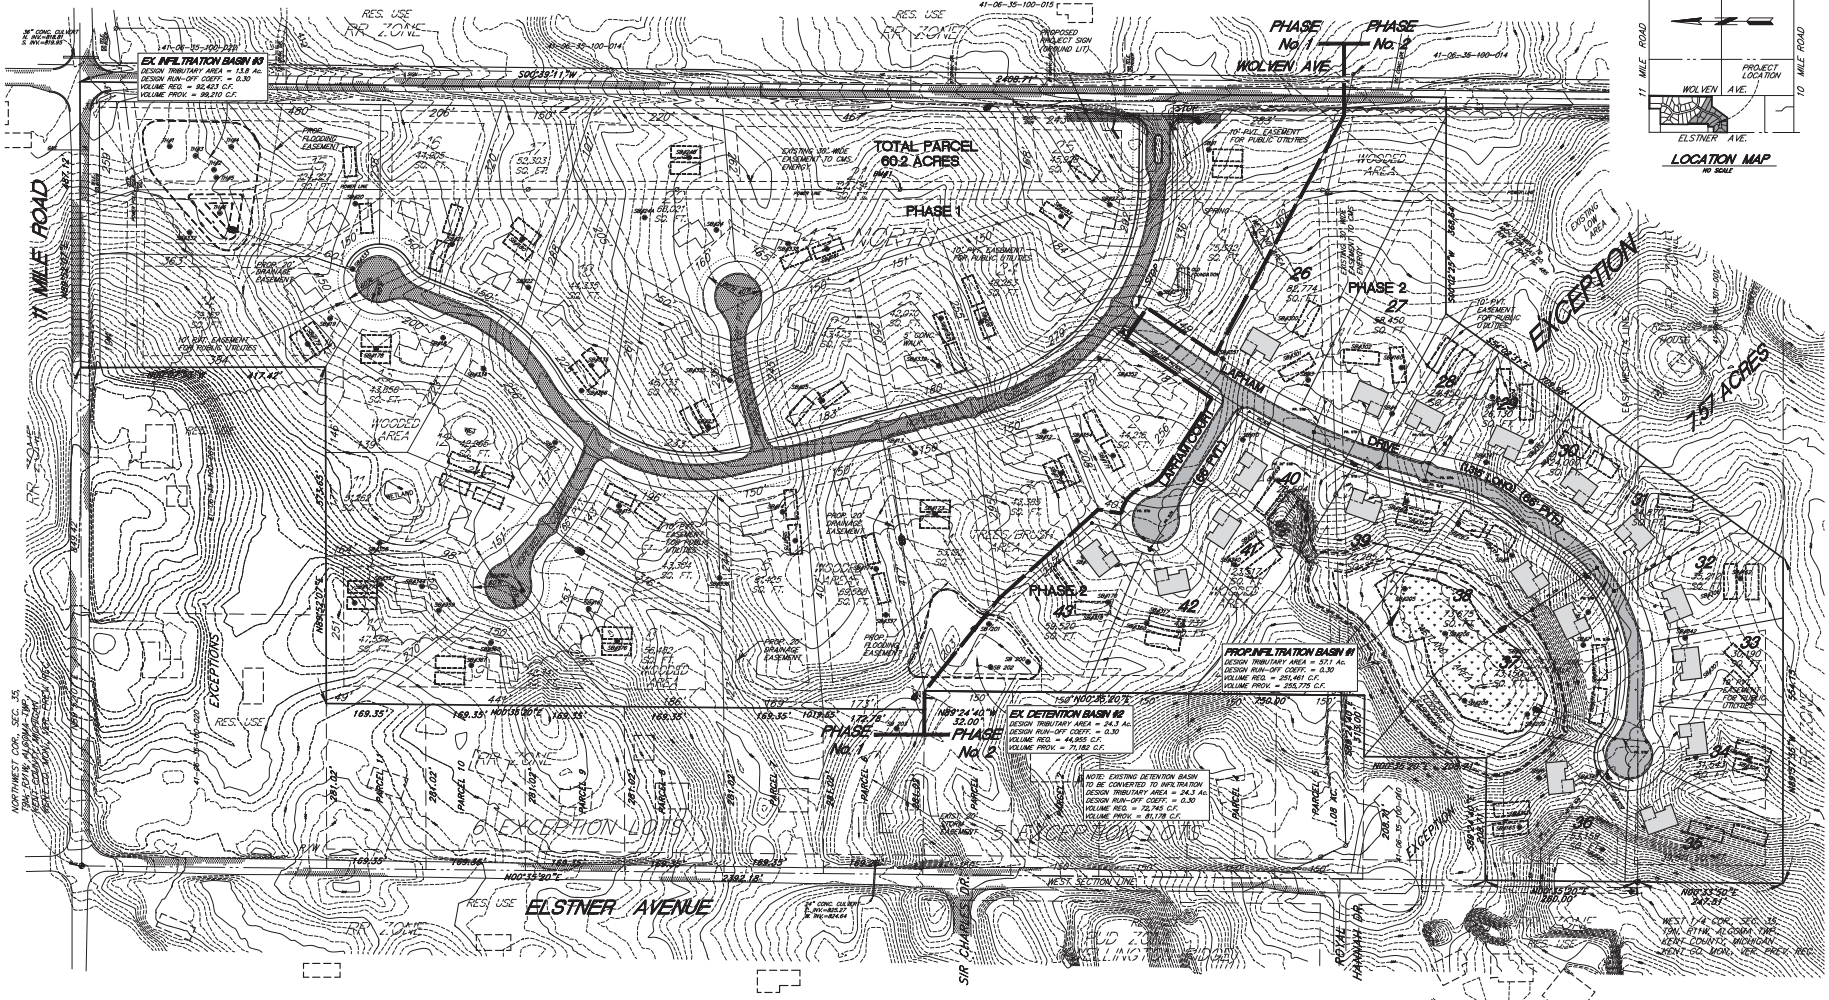

GENERAL NOTES:

1. "43 North" is a single family site condominium development. Units shall conform to the minimum lot requirements of the RR Zone.

2. Parcel number: 41-06-35-100-039

3. Address: 8927 Elstner Avenue, Rockford, Mi

4. Total Parcel Size = 60.2 acres (including r/w)

5. Property is currently zoned RR, and has the following minimum requirements:
- 150' lot width
- 42,000 sq. ft.
- 30' front yard setback
- 20' side yard setback
- 30' rear yard setback

6. Roads within the development are private, and shall conform to the Algoma Township private road ordinance. Total road length is approximately 4,135 lineal feet.

7. Units shall be served by public water and individual septic/drainfield systems as approved by the Kent County Health Department. Soil samples have been evaluated for each unit, and found suitable for individual drainfield use.

8. Street lights are not proposed for this development.

9 All storm water managment facilities will be designed in accordance with the Algoma Township Storm Water Ordinance. Piping shall consist of closed joint pipes. All proposed storm drainage and flooding easements shall be granted to the "43 North" condominium association.

10. Sidewalks are proposed for one side of the roads as shown on the site plan.

PHASE 2 LEGAL DESCRIPTION:

Part of the West 1/2 of Section 35, T9N, R11W, Algoma Township, Kent County, Michigan, described as: Commencing at the Northwest 1/4 corner of said Section; thence N89°52'07"E 1336.54 feet along the North line of said Section; thence S00°39'11"W 2155.19 feet along the East line of the West 1/2 of the Northwest 1/4 of said Section to the Place of Beginning; thence continuing S00°39'11"W 173.52 feet along the East line of the West 1/2 of the Northwest 1/4 of said Section; thence N89°57'35"W 368.64 feet; thence S35°57'29"W 709.98 feet; thence N89°57'35"W 554.15 feet parallel with the East-West 1/4 line of said Section; thence N00°33'50"E 247.51 feet along the West line of said Section to the West 1/4 corner of said Section; thence N00°35'20"E 260.00 feet along the West line of said Section; thence S89°24'40"E 208.71 feet; thence N00°35'20"E 208.71 feet parallel with the West line of said Section; thence S89°24'40"E 104.29 feet; thence N00°35'20"E 750.00 feet along the East line of the West 313.00 feet of the Northwest 1/4 of said Section; thence S51°07'59"E 202.74 feet; thence S41°52'26"E 227.00 feet; thence S10°11'01"W 39.50 feet; thence Southeasterly 66.96 feet along a 60.00 foot radius curve to the right, the long chord of which bears S47°50'36"E 63.54 feet; thence Southeasterly 35.79 feet along a 50.00 foot radius curve to the left, the long chord of which bears S36°22'40"E 35.03 feet; thence S56°53'05"E 153.03 feet; thence Northeasterly 33.15 feet along a 1233.00 foot radius curve to the right, the long chord of which bears N33°37'12"E 33.15 feet; thence N34°23'25"E 144.99 feet; thence S55°45'10"E 66.00 feet; thence S34°23'25"W 141.03 feet; thence S61°42'26"E 462.35 feet; thence S89°20'49"E 33.00 feet to the Place of Beginning. Subject to the road right of way for Wolven Avenue over the East 33.0 feet thereof. Contains 21.19 acres.

REVISIONS:
June 9, 2020 - Adjustments for Watermain

DRAWN BY: EP
APPROVED BY: FGH
DATE:
REVISIONS: May 13, 2015 - Owner Review
June 10, 2015 - For Bids
July 13, 2015 - For Permits
Aug 13, 2015 - For Township Eng.

SERVING THE NEEDS OF OUR CLIENTS SINCE 1987

Prein&Newhof
3055 PLAINFIELD AVE. NE
GRAND RAPIDS, MICHIGAN
TELE (616) 361-2223
FAX (616) 361-1093

OVERALL SITE PLAN FOR
"43 NORTH" SITE CONDOMINIUM
SECTION 35, T9N, R11W
ALGOMA TOWNSHIP, KENT COUNTY, MICHIGAN

CLIENT:
DALE KRAKER
WOLVEN INVESTMENTS, LLC
3115 RAILWAY DRIVE
BYRON CENTER, MICHIGAN 49315

PROJECT NO.
200042-P1

SHEET
1 of 7